
PLANIMETRIA STRINGATURA - Scala 1:500

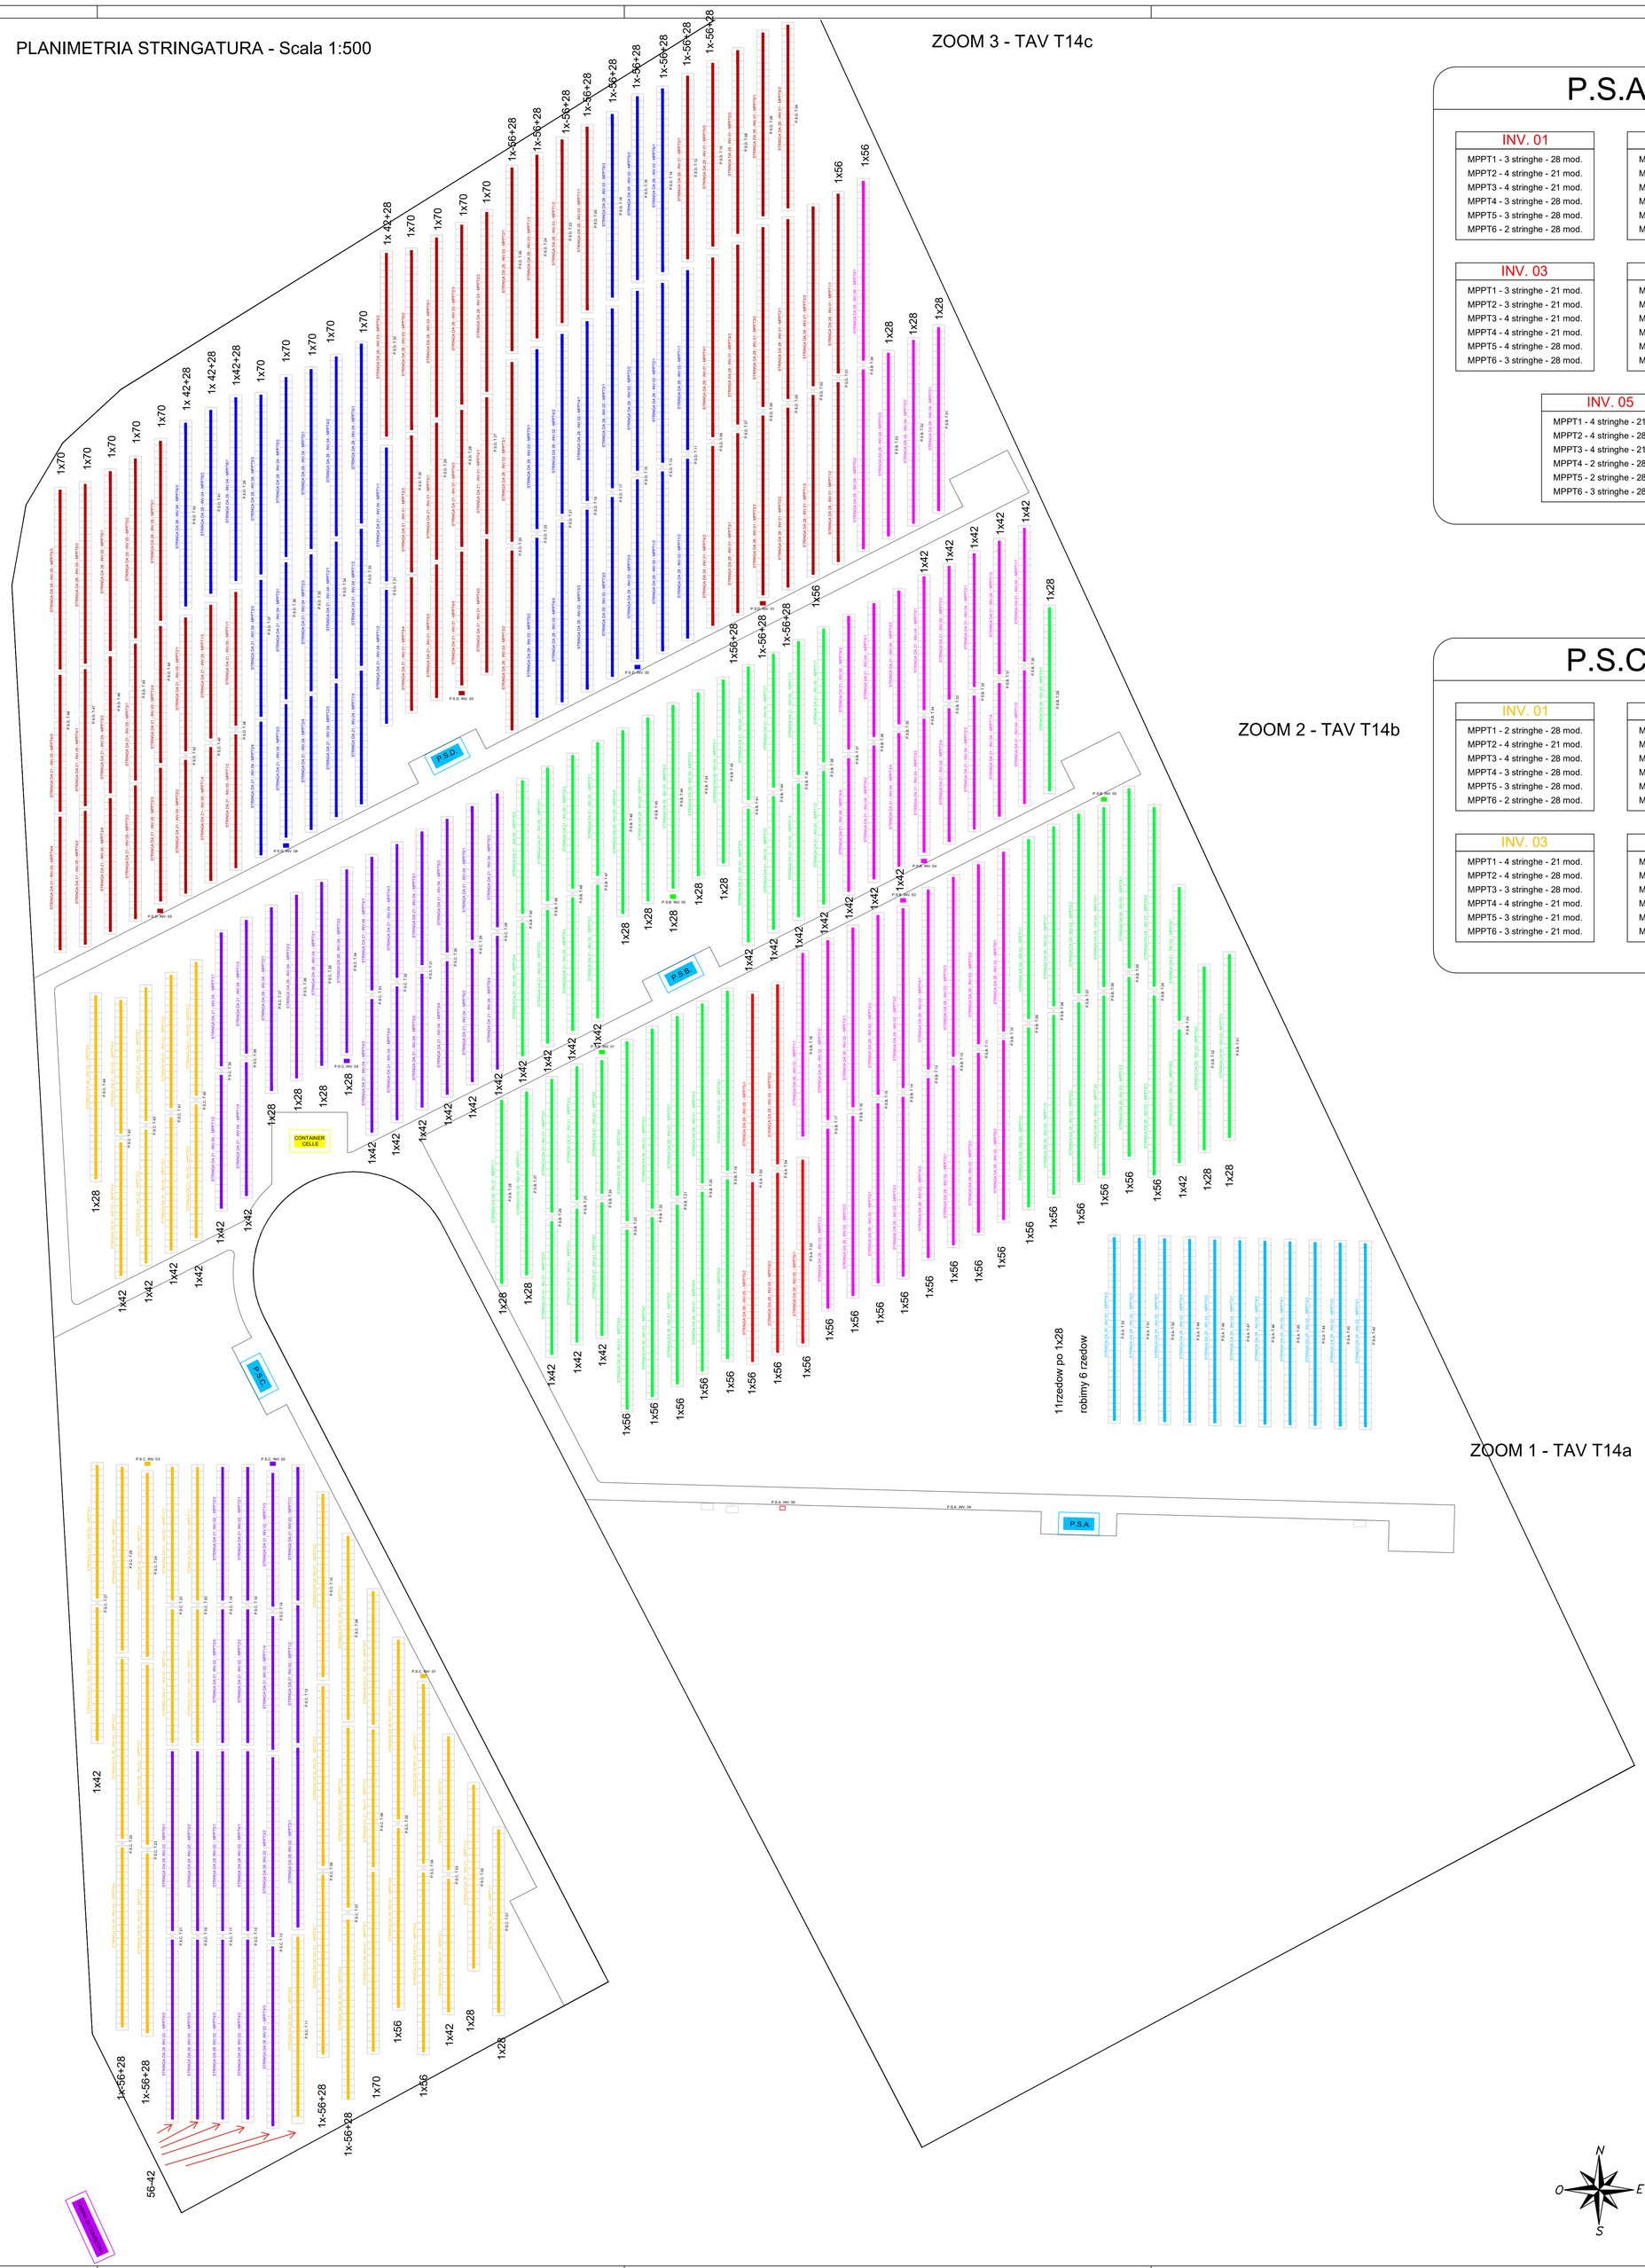

P.S.A.

INV. 01
MPPT1 - 3 stringhe - 28 mod.
MPPT2 - 4 stringhe - 21 mod.
MPPT3 - 4 stringhe - 21 mod.
MPPT4 - 3 stringhe - 28 mod.
MPPT5 - 3 stringhe - 28 mod.
MPPT6 - 2 stringhe - 28 mod.

INV. 02
MPPT1 - 3 stringhe - 28 mod.
MPPT2 - 3 stringhe - 28 mod.
MPPT3 - 3 stringhe - 28 mod.
MPPT4 - 2 stringhe - 28 mod.
MPPT5 - 3 stringhe - 28 mod.
MPPT6 - 3 stringhe - 28 mod.

INV. 03
MPPT1 - 3 stringhe - 21 mod.
MPPT2 - 3 stringhe - 21 mod.
MPPT3 - 4 stringhe - 21 mod.
MPPT4 - 4 stringhe - 21 mod.
MPPT5 - 4 stringhe - 28 mod.
MPPT6 - 3 stringhe - 28 mod.

INV. 04
MPPT1 - 3 stringhe - 28 mod.
MPPT2 - 3 stringhe - 28 mod.
MPPT3 - 3 stringhe - 28 mod.
MPPT4 - 3 stringhe - 28 mod.
MPPT5 - 3 stringhe - 28 mod.
MPPT6 - 2 stringhe - 28 mod.

INV. 05
MPPT1 - 4 stringhe - 21 mod.
MPPT2 - 4 stringhe - 28 mod.
MPPT3 - 4 stringhe - 21 mod.
MPPT4 - 2 stringhe - 28 mod.
MPPT5 - 2 stringhe - 28 mod.
MPPT6 - 3 stringhe - 28 mod.

P.S.B.

INV. 01
MPPT1 - 2 stringhe - 28 mod.
MPPT2 - 3 stringhe - 21 mod.
MPPT3 - 3 stringhe - 21 mod.
MPPT4 - 3 stringhe - 28 mod.
MPPT5 - 3 stringhe - 28 mod.
MPPT6 - 4 stringhe - 28 mod.

INV. 02
MPPT1 - 3 stringhe - 28 mod.
MPPT2 - 3 stringhe - 28 mod.
MPPT3 - 3 stringhe - 28 mod.
MPPT4 - 3 stringhe - 28 mod.
MPPT5 - 3 stringhe - 28 mod.
MPPT6 - 2 stringhe - 28 mod.

INV. 03
MPPT1 - 3 stringhe - 28 mod.
MPPT2 - 3 stringhe - 28 mod.
MPPT3 - 3 stringhe - 28 mod.
MPPT4 - 3 stringhe - 28 mod.
MPPT5 - 3 stringhe - 28 mod.
MPPT6 - 2 stringhe - 21 mod.

INV. 04
MPPT1 - 4 stringhe - 21 mod.
MPPT2 - 4 stringhe - 21 mod.
MPPT3 - 4 stringhe - 21 mod.
MPPT4 - 4 stringhe - 21 mod.
MPPT5 - 3 stringhe - 28 mod.
MPPT6 - 2 stringhe - 28 mod.

INV. 05
MPPT1 - 4 stringhe - 21 mod.
MPPT2 - 4 stringhe - 21 mod.
MPPT3 - 3 stringhe - 28 mod.
MPPT4 - 2 stringhe - 28 mod.
MPPT5 - 4 stringhe - 21 mod.
MPPT6 - 4 stringhe - 21 mod.

P.S.C.

INV. 01
MPPT1 - 2 stringhe - 28 mod.
MPPT2 - 4 stringhe - 21 mod.
MPPT3 - 4 stringhe - 28 mod.
MPPT4 - 3 stringhe - 28 mod.
MPPT5 - 3 stringhe - 28 mod.
MPPT6 - 2 stringhe - 28 mod.

INV. 02
MPPT1 - 4 stringhe - 21 mod.
MPPT2 - 4 stringhe - 21 mod.
MPPT3 - 3 stringhe - 28 mod.
MPPT4 - 3 stringhe - 28 mod.
MPPT5 - 3 stringhe - 28 mod.
MPPT6 - 2 stringhe - 28 mod.

INV. 03
MPPT1 - 4 stringhe - 21 mod.
MPPT2 - 4 stringhe - 28 mod.
MPPT3 - 3 stringhe - 28 mod.
MPPT4 - 4 stringhe - 21 mod.
MPPT5 - 3 stringhe - 21 mod.
MPPT6 - 3 stringhe - 21 mod.

INV. 04
MPPT1 - 4 stringhe - 21 mod.
MPPT2 - 2 stringhe - 28 mod.
MPPT3 - 2 stringhe - 28 mod.
MPPT4 - 4 stringhe - 21 mod.
MPPT5 - 4 stringhe - 21 mod.
MPPT6 - 4 stringhe - 21 mod.

P.S.D.

INV. 01
MPPT1 - 3 stringhe - 28 mod.
MPPT2 - 3 stringhe - 28 mod.
MPPT3 - 3 stringhe - 28 mod.
MPPT4 - 3 stringhe - 28 mod.
MPPT5 - 3 stringhe - 28 mod.
MPPT6 - 2 stringhe - 28 mod.

INV. 02
MPPT1 - 3 stringhe - 28 mod.
MPPT2 - 3 stringhe - 28 mod.
MPPT3 - 3 stringhe - 28 mod.
MPPT4 - 3 stringhe - 28 mod.
MPPT5 - 2 stringhe - 28 mod.
MPPT6 - 3 stringhe - 28 mod.

INV. 03
MPPT1 - 3 stringhe - 28 mod.
MPPT2 - 3 stringhe - 28 mod.
MPPT3 - 2 stringhe - 28 mod.
MPPT4 - 4 stringhe - 21 mod.
MPPT5 - 4 stringhe - 21 mod.
MPPT6 - 3 stringhe - 28 mod.

INV. 04
MPPT1 - 4 stringhe - 21 mod.
MPPT2 - 4 stringhe - 21 mod.
MPPT3 - 4 stringhe - 21 mod.
MPPT4 - 2 stringhe - 28 mod.
MPPT5 - 3 stringhe - 28 mod.
MPPT6 - 3 stringhe - 28 mod.

INV. 05
MPPT1 - 4 stringhe - 21 mod.
MPPT2 - 4 stringhe - 21 mod.
MPPT3 - 4 stringhe - 21 mod.
MPPT4 - 4 stringhe - 21 mod.
MPPT5 - 2 stringhe - 28 mod.
MPPT6 - 3 stringhe - 28 mod.

COMUNE DI MOMO
Provincia di Novara

Committente

RF-GIULIETTA SRL
Via Bottonaga, 4
25125 BRESCIA (BS)
P.iva /C.F. 04364160988

EPC

SOLEVENTO ENERGIE • RINNOVABILI

Progetto

Progetto esecutivo per la realizzazione di un nuovo impianto fotovoltaico a terra denominato "RF-GIULIETTA" di potenza pari a 6,4915 MWp e relativo elettrodotto per la connessione alla RTN

Ubicazione intervento

STRADA VICINALE VERNINO - 28015 MOMO (NO)

Il tecnico incaricato

Il direttore incaricato

ORDINE DEGLI INGEGNERI DELLA PROVINCIA DI BRESCIA
A 1657
Ingegnere
PIETRO CASTIONI
Civile ed Ambientale
Industriale
dell'Informazione

SISTHEMA Engineering

SISTHEMA ENGINEERING S.R.L.
Società di Ingegneria Integrata
4, via Bottonaga - 25125
Brescia, (Bs) Italia

CertI. n° 32165

Codice documento

004_26_PE_T14

Titolo documento

PLANIMETRIA STRINGATURA

Revisione Elaborato

N. REV.	DATA REV.	DESCRIZIONE REVISIONE	REDAZIONE	APPROVAZIONE
0	05/2026	Prima emissione	AG	PC